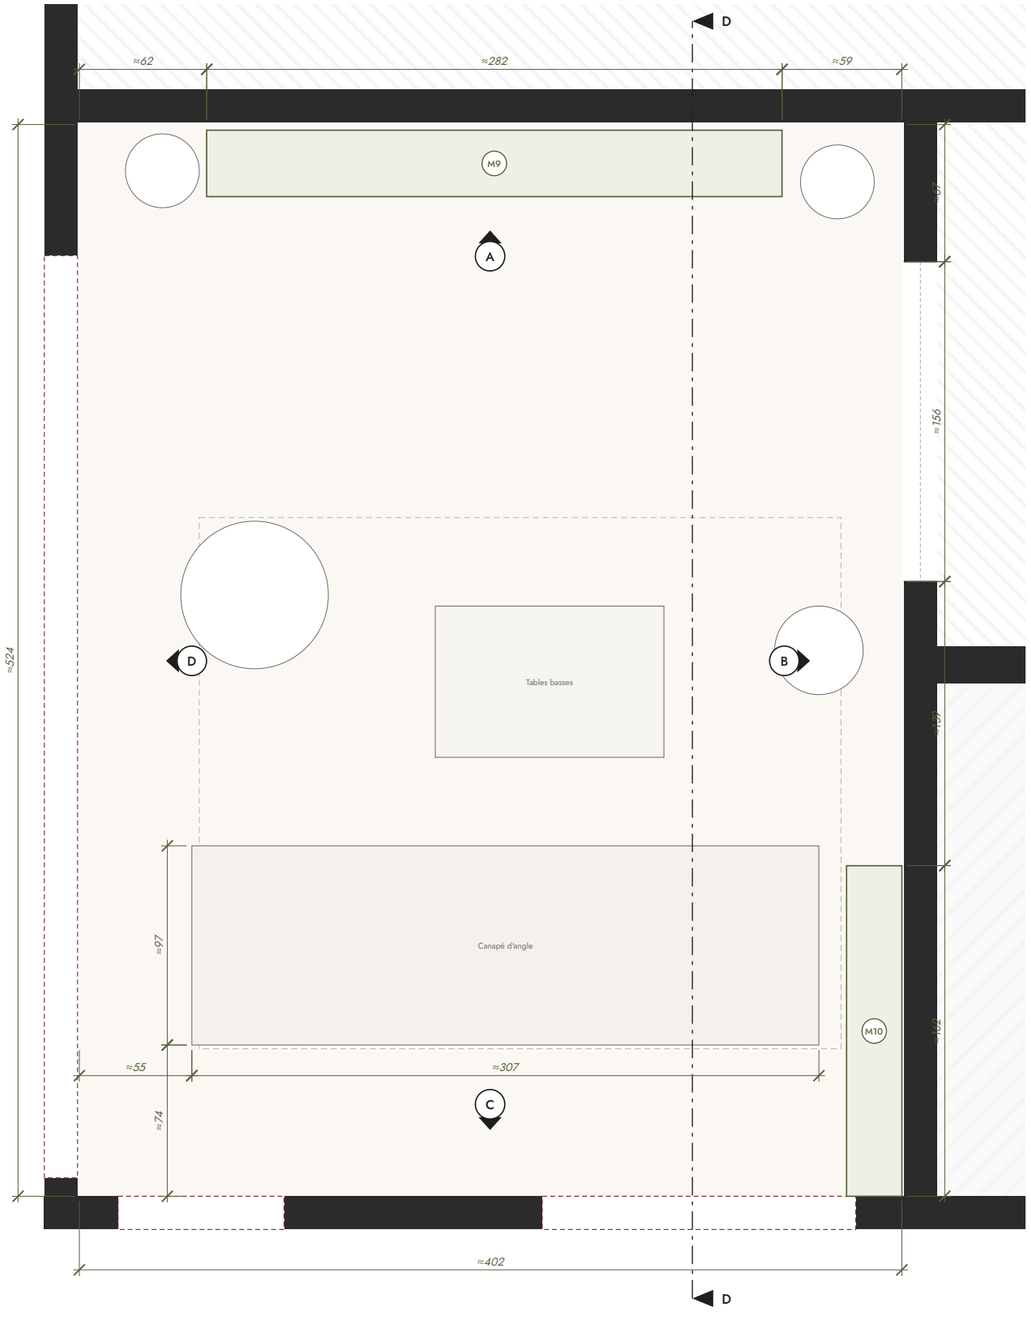

SÉJOUR DE L'ÉTAGE

Niveau	ÉTAGE 1
Surface	*≈ 21,1 m²*
Hauteur sous faux-plafond	*≈ 289*
Plafond central	**à confirmer**
Sol fini	**à confirmer**

Repères A, B, C… : murs dessinés en élévation. Traits mixtes : coupes. M… : mobilier sur mesure.

1 PLAN COTÉ — SÉJOUR DE L'ÉTAGE 1:30

KAÏRA INTERIOR DESIGN

KAÏRA INTERIOR DESIGN
Architecture intérieure

PROJET
Villa — Rez-de-chaussée & Étage 1

DOCUMENT
Dossier technique d'architecture intérieure

NIVEAU · PIÈCE
ÉTAGE 1 · Séjour étage 1

TITRE DE LA PLANCHE
Plan coté — Séjour étage 1

ÉCHELLE	FORMAT
1:30	A3
DATE	INDICE
11.11.2026	A

424	cote vérifiée (plan source)
≈ 59	cote déduite (relevé)
À CONF.	cote à confirmer

Cotes en cm. Ne pas mesurer sur le dessin. Toutes les cotes sont à vérifier sur site avant exécution.

N° DE DESSIN
KAI-VIL-400

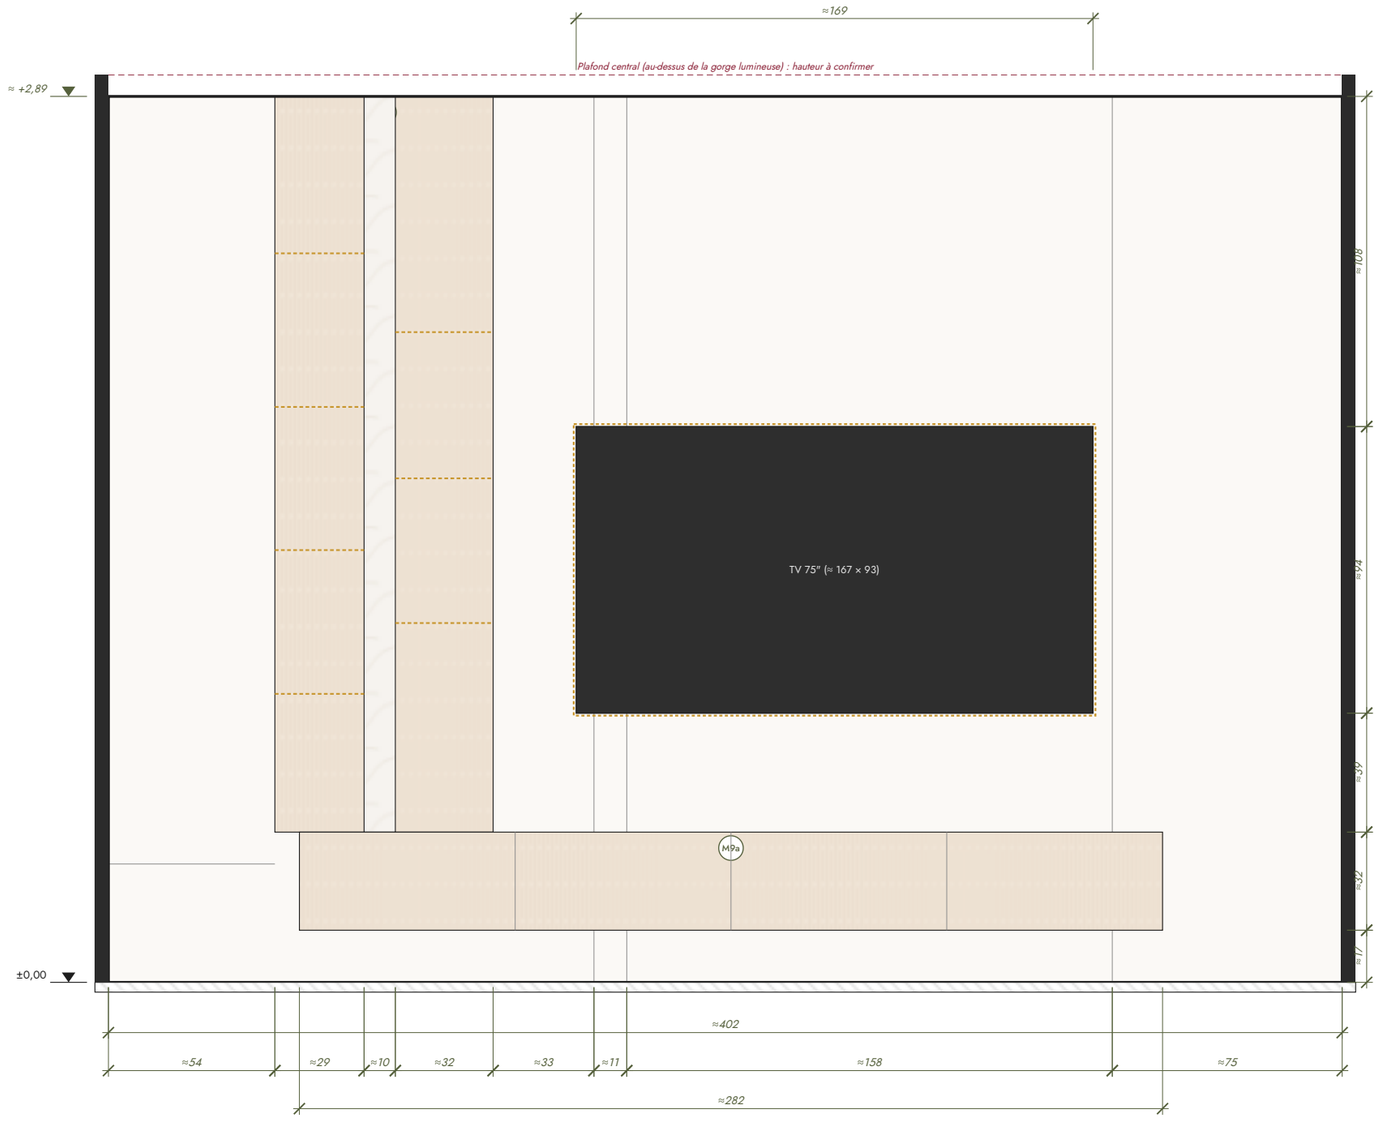

A MUR A — NORD (MUR TV)

1:20

MUR A — NOTES

- Source : etage1-sejour-01. Calibrage : Largeur 402,5 relevée sur la vue de dessus ; téléviseur 75" contrôlé (168,6 × 93,6).
- M9a : meuble suspendu chêne, 4 façades, profondeur ≈ 32 (vue de dessus).
- M9b : étagère verticale chêne éclairée, montant central marbre ; tablettes à ±5.
- Panneaux muraux crème à joints creux.

PLAN DE REPÉRAGE

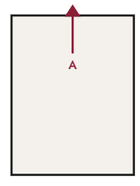

KAÏRA INTERIOR DESIGN

Architecture intérieure

PROJET
Villa — Rez-de-chaussée & Étage 1

DOCUMENT
Dossier technique d'architecture intérieure

NIVEAU · PIÈCE
ÉTAGE 1 · Séjour étage 1

TITRE DE LA PLANCHE
Élévation A — Séjour étage 1

ÉCHELLE	FORMAT
1:20	A3
DATE	INDICE
11.11.2026	A

424	cote vérifiée (plan source)
≈ 59	cote déduite (relevé)
À CONF.	cote à confirmer

Cotes en cm. Ne pas mesurer sur le dessin. Toutes les cotes sont à vérifier sur site avant exécution.

N° DE DESSIN
KAI-VIL-401

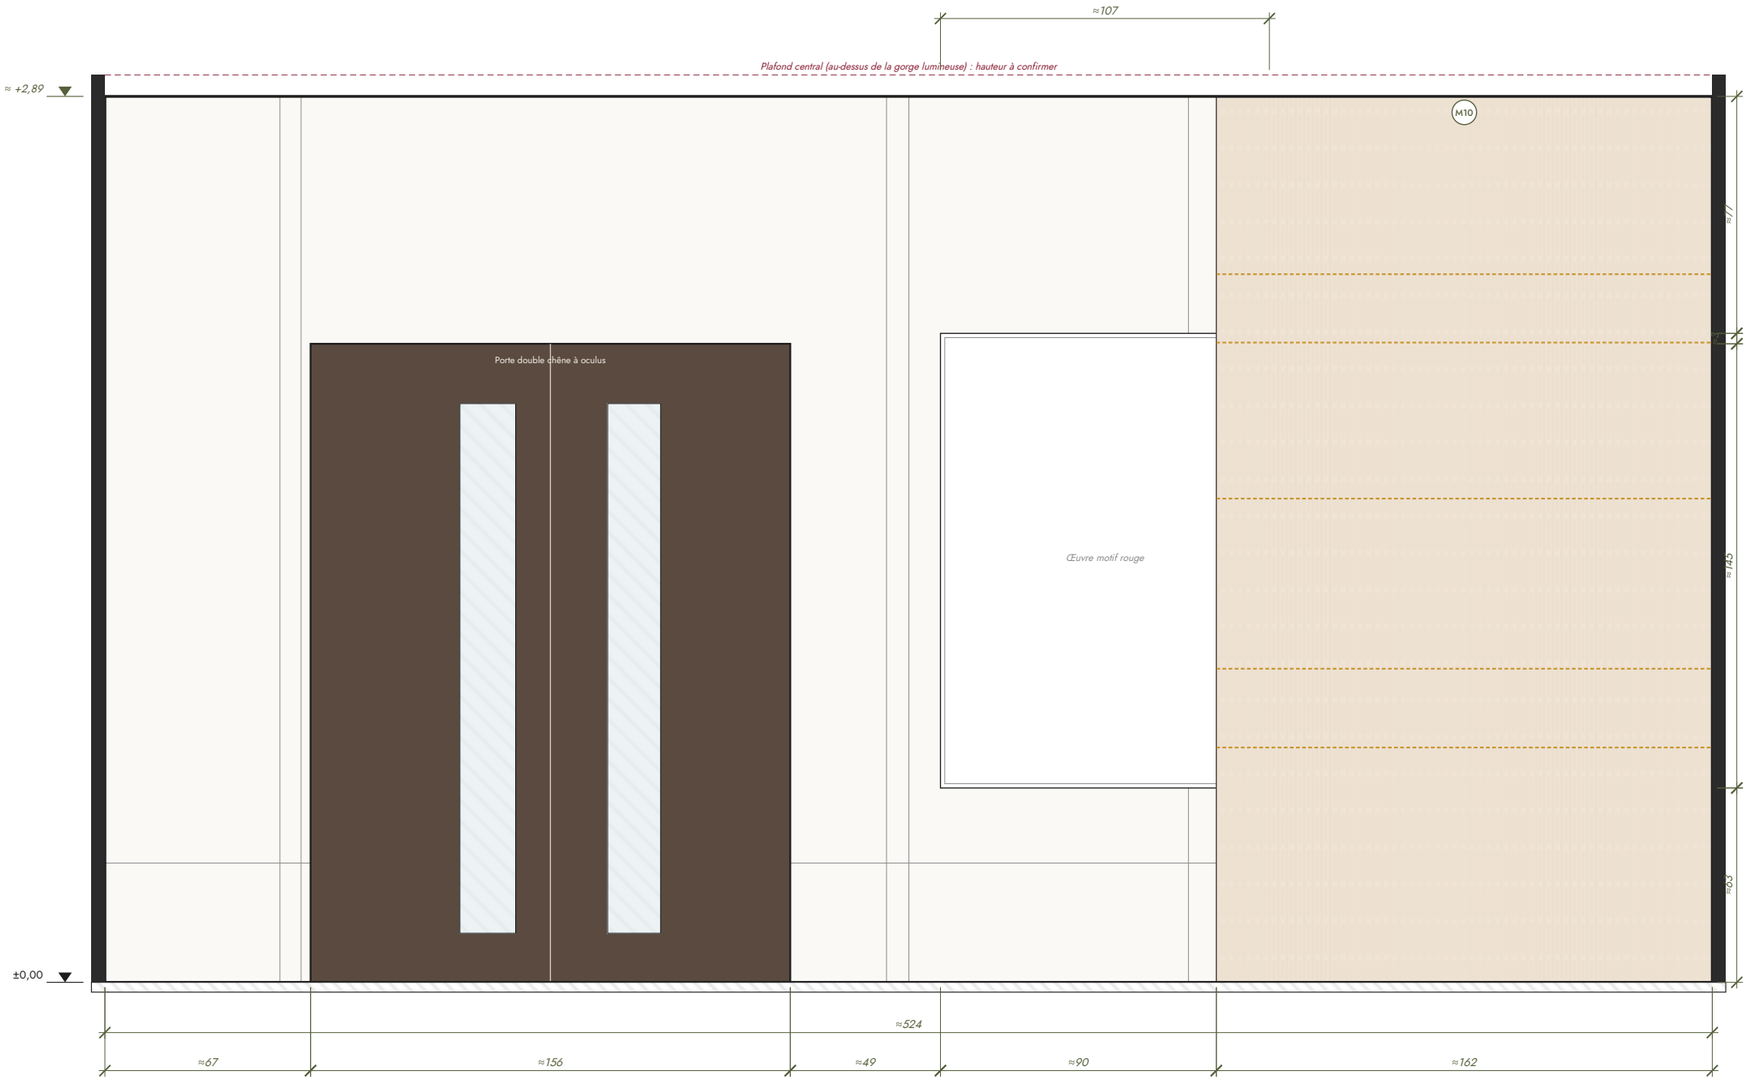

B **MUR B — EST (MUR D'ENTRÉE)**

1:20

MUR B — NOTES

- Source : etage1-sejour-08. Calibrage : Longueur 524,4 (vue de dessus) ; hauteur reprise du mur A.
- Porte double : ≈ 156 × 208, deux oculus vitrés verticaux ; sens d'ouverture à confirmer.
- M10 : bibliothèque chêne éclairée, profondeur ≈ 27 ; tablettes relevées à ±5.

PLAN DE REPÉRAGE

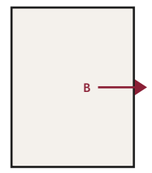

KAÏRA INTERIOR DESIGN

Architecture intérieure

PROJET
Villa — Rez-de-chaussée & Étage 1

DOCUMENT
Dossier technique d'architecture intérieure

NIVEAU · PIÈCE
ÉTAGE 1 · Séjour étage 1

TITRE DE LA PLANCHE
Élévation B — Séjour étage 1

ÉCHELLE	FORMAT
1:20	A3
DATE	INDICE
11.11.2026	A

424	cote vérifiée (plan source)
≈ 59	cote déduite (relevé)
À CONF.	cote à confirmer

Cotes en cm. Ne pas mesurer sur le dessin. Toutes les cotes sont à vérifier sur site avant exécution.

N° DE DESSIN
KAI-VIL-402

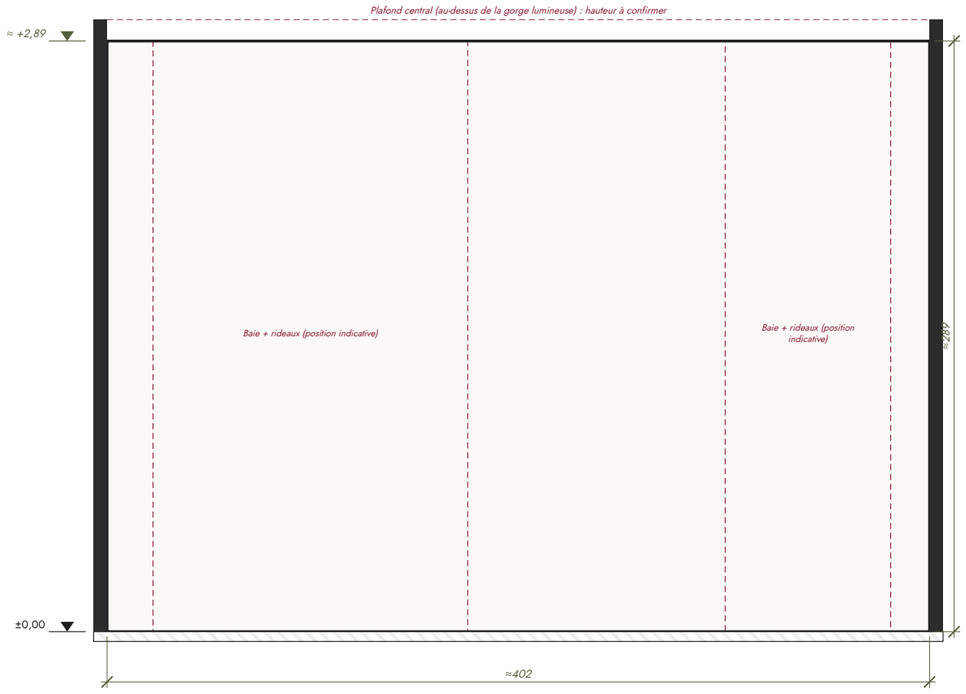

C MUR C — SUD (FENÊTRES) 1:30

D MUR D — OUEST (FENÊTRES) 1:30

MUR C — NOTES

- Source : etage1-sejour-02 (vue de 3/4). Calibrage : Largeur relevée sur la vue de dessus.
- Baies du mur sud : positions déduites des rideaux de la maquette ; largeurs, allèges et linteaux à confirmer.

MUR D — NOTES

- Source : etage1-sejour-03 (vue de 3/4). Calibrage : Longueur relevée sur la vue de dessus.
- Nombre, largeurs et hauteurs des baies du mur ouest : à confirmer.

PLAN DE REPÉRAGE

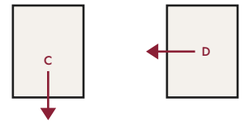

KAÏRA INTERIOR DESIGN

Architecture intérieure

PROJET
Villa — Rez-de-chaussée & Étage 1

DOCUMENT
Dossier technique d'architecture intérieure

NIVEAU · PIÈCE
ÉTAGE 1 · Séjour étage 1

TITRE DE LA PLANCHE
Élévations C et D — Séjour étage 1

ÉCHELLE	FORMAT
1:30	A3
DATE	INDICE
11.11.2026	A

424	cote vérifiée (plan source)
≈ *59*	cote déduite (relevé)
À CONF.	cote à confirmer

Cotes en cm. Ne pas mesurer sur le dessin. Toutes les cotes sont à vérifier sur site avant exécution.

N° DE DESSIN
KAI-VIL-403

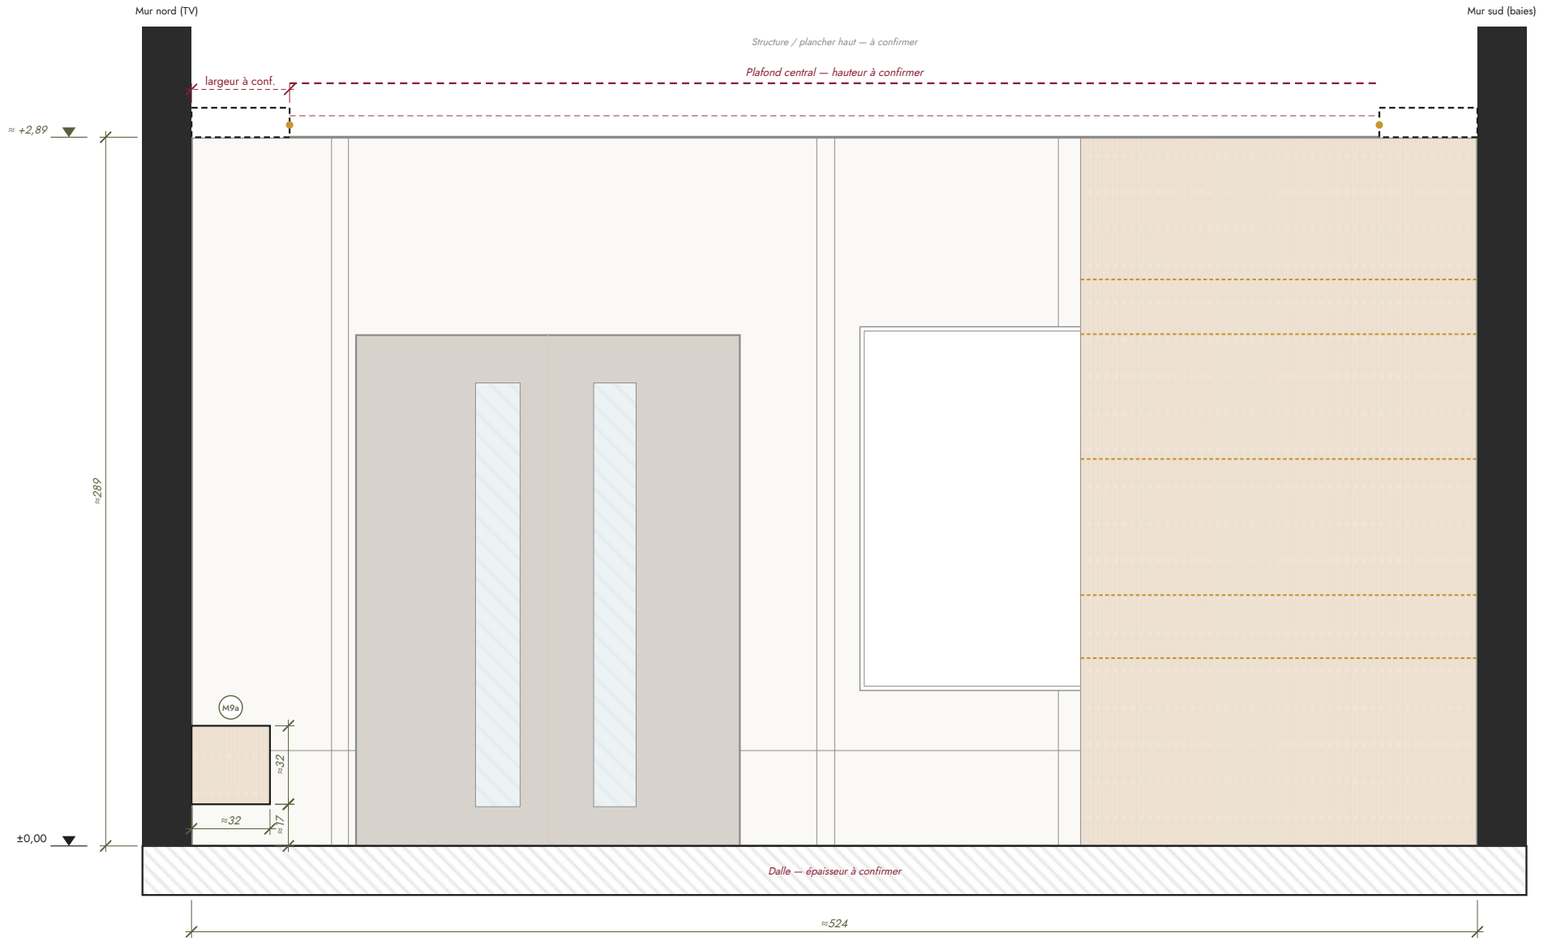

D COUPE DD — SÉJOUR DE L'ÉTAGE (NORD-SUD, VUE VERS L'EST) 1:25

NOTES

- Coupe établie à partir des hauteurs déduites ; l'élévation vue au-delà est dessinée en gris.
- Retombée périphérique de faux-plafond avec gorge lumineuse LED : largeur à confirmer.
- Plafond central, plancher haut et épaisseur de dalle : à confirmer.
- Mobilier coupé : profils relevés (vue de dessus pour la profondeur, rendus pour les hauteurs).

KAÏRA INTERIOR DESIGN

KAÏRA INTERIOR DESIGN
Architecture intérieure

PROJET
Villa — Rez-de-chaussée & Étage 1

DOCUMENT
Dossier technique d'architecture intérieure

NIVEAU · PIÈCE
ÉTAGE 1 · Séjour étage 1

TITRE DE LA PLANCHE
Coupe DD — Séjour étage 1

ÉCHELLE	FORMAT
1:25	A3
DATE	INDICE
11.11.2026	A

424	cote vérifiée (plan source)
≈ 59	cote déduite (relevé)
À CONF.	cote à confirmer

Cotes en cm. Ne pas mesurer sur le dessin. Toutes les cotes sont à vérifier sur site avant exécution.

N° DE DESSIN
KAI-VIL-404

Planche 40 / 58

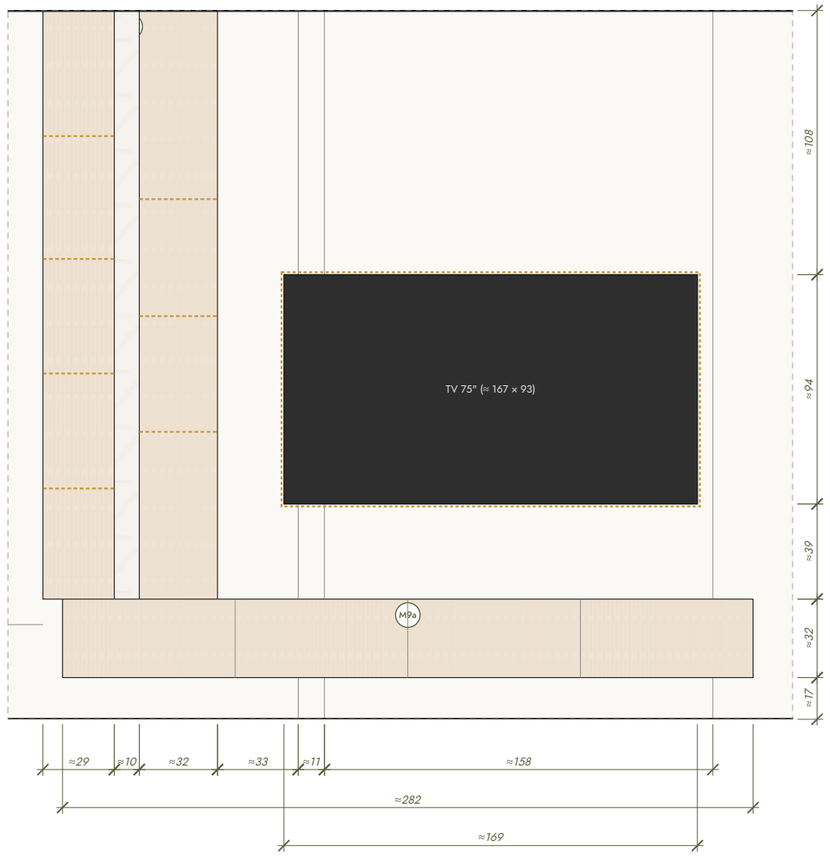

M9a **M9A + M9B — VUE DE FACE (EXTRAIT MUR A)** 1:25

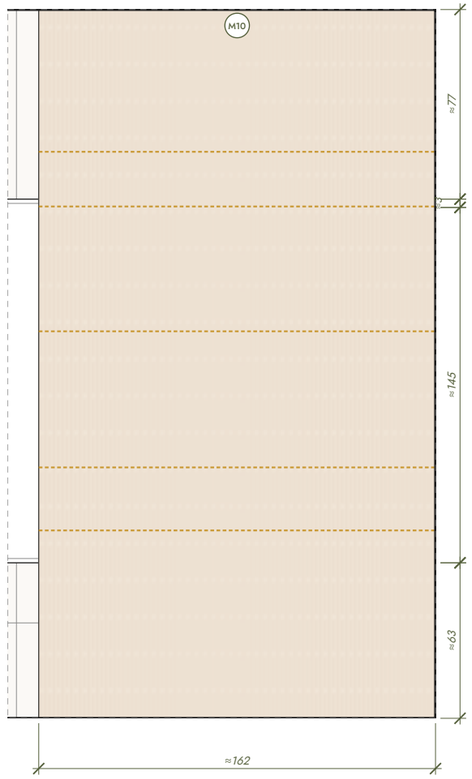

M10 **M10 — VUE DE FACE (EXTRAIT MUR B)** 1:25

NOMENCLATURE DU MOBILIER SUR MESURE

RÉF.	DÉSIGNATION	DIMENSIONS (CM)	OBSERVATIONS
M9a	Meuble TV suspendu chêne	*L ≈ 282 · P ≈ 32 · H ≈ 32 · pose ≈ 17*	4 façades égales
M9b	Étagère verticale éclairée, montant marbre	*L ≈ 71 ·* **P à conf.** *· H ≈ 240*	posée sur M9a ; 7 tablettes éclairées
M10	Bibliothèque chêne éclairée (mur d'entrée)	*L ≈ 162 · P ≈ 27 · H ≈ 289*	soubassement fermé ≈ 70 ; tablettes éclairées

L = longueur, P = profondeur, H = hauteur, pose = hauteur sous meuble. Dimensions ≈ relevées sur la vue de dessus (L, P) et sur les rendus de face (H). Quincaillerie, épaisseurs de panneaux, structure et détails d'assemblage : à définir en plans d'exécution.

KAÏRA INTERIOR DESIGN

KAÏRA INTERIOR DESIGN
Architecture intérieure

PROJET
Villa — Rez-de-chaussée & Étage 1

DOCUMENT
Dossier technique d'architecture intérieure

NIVEAU · PIÈCE
ÉTAGE 1 · Séjour étage 1

TITRE DE LA PLANCHE
Mobilier sur mesure — Séjour étage 1

ÉCHELLE
1:25

FORMAT
A3

DATE
11.11.2026

INDICE
A

424	cote vérifiée (plan source)
≈ 59	cote déduite (relevé)
À CONF.	cote à confirmer

Cotes en cm. Ne pas mesurer sur le dessin. Toutes les cotes sont à vérifier sur site avant exécution.

N° DE DESSIN
KAI-VIL-405

MATÉRIAUX ET FINITIONS — SÉJOUR DE L'ÉTAGE

	MATÉRIAU	LOCALISATION	TEINTE RELEVÉE	RÉFÉRENCE FABRICANT	FINITION
	Chêne	Meuble TV, étagère, bibliothèque, porte double	#563C27	à confirmer	à confirmer
	Marbre blanc veiné	Montant de l'étagère, table basse	#877B6D	à confirmer	à confirmer
	Panneaux crème à joints creux	Murs	#756758	à confirmer	à confirmer
	Tissu gris taupe	Canapé d'angle, fauteuil	#685E4D	à confirmer	à confirmer
	Cuir cognac	Pouf à côtes, coussins	#503726	à confirmer	à confirmer
	Tapis tissé	Sol du salon	#8D837A	à confirmer	à confirmer
	Parquet bois	Sol	#745B45	à confirmer	à confirmer
	Rideaux taupe + voilage	Baies	#786557	à confirmer	à confirmer
	Œuvre motif rouge	Mur d'entrée	#7B3931	à confirmer	à confirmer

NOTES

- Matériaux identifiés sur les rendus 3D du projet ; aucune référence n'est inventée.
- Teinte relevée : médiane des pixels d'une zone du rendu. Indicative : elle dépend de l'éclairage de la scène.
- « — » : teinte non relevable sur le rendu (reflets, lumière, métal).
- À valider avant commande : échantillons physiques, références fabricants, finitions (mat, satiné, brossé, adouci…), sens du fil et calepinage des panneaux bois et marbre.
- Éclairage : température de couleur et intensité des LED à définir (non mesurables sur les rendus).

KAÏRA INTERIOR DESIGN

KAÏRA INTERIOR DESIGN
Architecture intérieure

PROJET
Villa — Rez-de-chaussée & Étage 1

DOCUMENT
Dossier technique d'architecture intérieure

NIVEAU · PIÈCE
ÉTAGE 1 · Séjour étage 1

TITRE DE LA PLANCHE
Matériaux et finitions — Séjour étage 1

ÉCHELLE
—

FORMAT
A3

DATE
11.11.2026

INDICE
A

424 cote vérifiée (plan source)
≈ *59* cote déduite (relevé)
À CONF. cote à confirmer

Cotes en cm. Ne pas mesurer sur le dessin. Toutes les cotes sont à vérifier sur site avant exécution.

N° DE DESSIN
KAI-VIL-406

SÉJOUR DE L'ÉTAGE

Salon — vers les baies du mur sud

Fichier : etage1-sejour-02.png — rendu 3D original KAÏRA, inséré en entier, sans recadrage ni retouche.

REPÉRAGE — MUR C

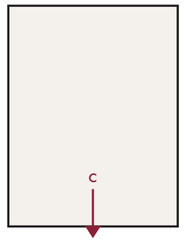

KAÏRA INTERIOR DESIGN

Architecture intérieure

PROJET
Villa — Rez-de-chaussée & Étage 1

DOCUMENT
Dossier technique d'architecture intérieure

NIVEAU · PIÈCE
ÉTAGE 1 · Séjour étage 1

TITRE DE LA PLANCHE
Rendu 3D — Séjour étage 1

ÉCHELLE	FORMAT
—	A3
DATE	INDICE
11.11.2026	A

424	cote vérifiée (plan source)
≈ 59	cote déduite (relevé)
À CONF.	cote à confirmer

Cotes en cm. Ne pas mesurer sur le dessin. Toutes les cotes sont à vérifier sur site avant exécution.

N° DE DESSIN
KAI-VIL-407

etage1-sejour-01 — Mur A — mur TV (vue de face)

etage1-sejour-05 — Mur A — mur TV (vue de 3/4)

KAÏRA
INTERIOR DESIGN

KAÏRA INTERIOR DESIGN
Architecture intérieure

PROJET
Villa — Rez-de-chaussée & Étage 1

DOCUMENT
Dossier technique d'architecture intérieure

NIVEAU · PIÈCE
ÉTAGE 1 · Séjour étage 1

TITRE DE LA PLANCHE
Rendus 3D — Séjour étage 1 (1/4)

ÉCHELLE	FORMAT
—	A3
DATE	**INDICE**
11.11.2026	A

424	cote vérifiée (plan source)
≈ 59	cote déduite (relevé)
À CONF.	cote à confirmer

Cotes en cm. Ne pas mesurer sur le dessin. Toutes les cotes sont à vérifier sur site avant exécution.

N° DE DESSIN
KAI-VIL-408

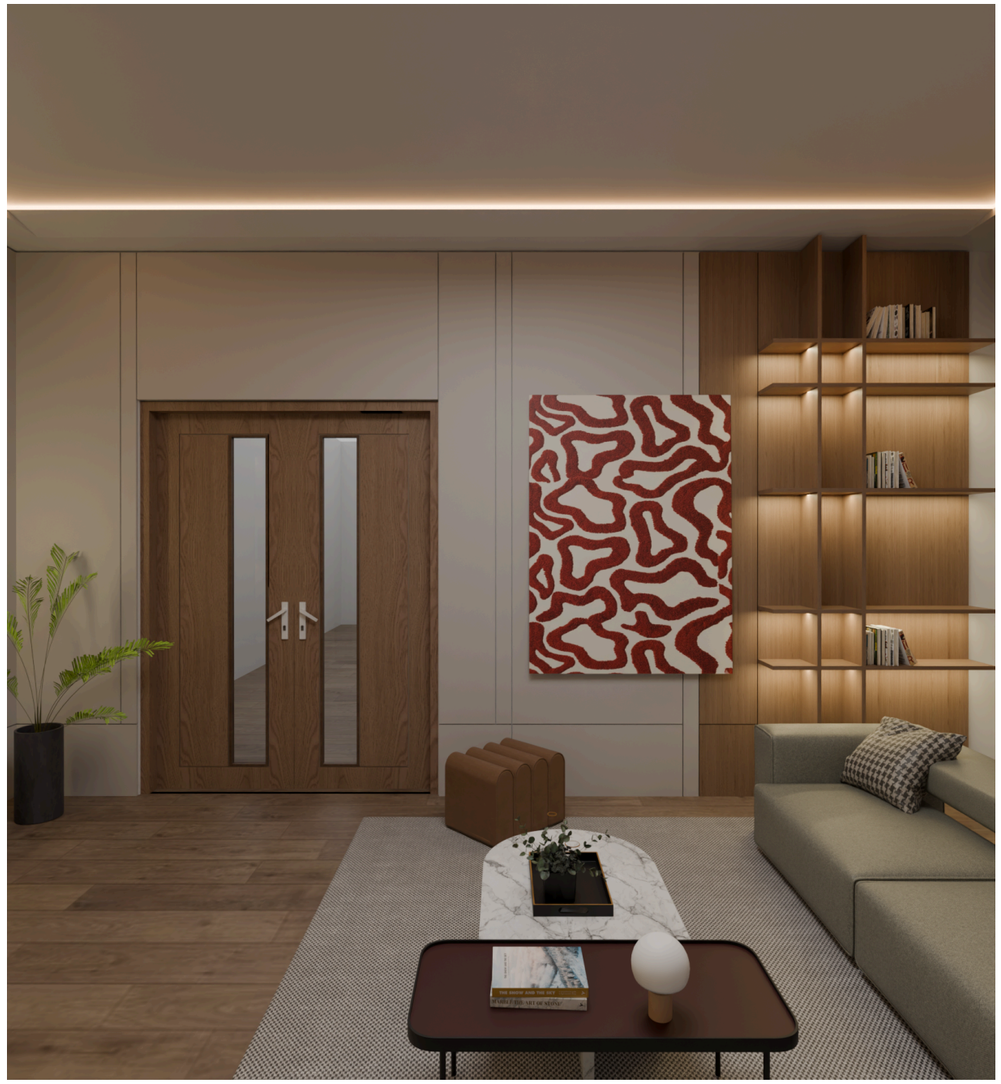

etage1-sejour-08 — Mur B — mur d'entrée (vue de face)

etage1-sejour-06 — Mur B — mur d'entrée (vue de 3/4)

KAÏRA
INTERIOR DESIGN

KAÏRA INTERIOR DESIGN
Architecture intérieure

PROJET
Villa — Rez-de-chaussée & Étage 1

DOCUMENT
Dossier technique d'architecture intérieure

NIVEAU · PIÈCE
ÉTAGE 1 · Séjour étage 1

TITRE DE LA PLANCHE
Rendus 3D — Séjour étage 1 (2/4)

ÉCHELLE	FORMAT
—	A3
DATE	**INDICE**
11.11.2026	A

424	cote vérifiée (plan source)
≈ 59	cote déduite (relevé)
À CONF.	cote à confirmer

Cotes en cm. Ne pas mesurer sur le dessin. Toutes les cotes sont à vérifier sur site avant exécution.

N° DE DESSIN
KAI-VIL-409

etage1-sejour-09 — Mur B — depuis le canapé (vue de 3/4)

etage1-sejour-03 — Salon — vers le sud-ouest (vue de 3/4)

KAÏRA
INTERIOR DESIGN

KAÏRA INTERIOR DESIGN
Architecture intérieure

PROJET
Villa — Rez-de-chaussée & Étage 1

DOCUMENT
Dossier technique d'architecture intérieure

NIVEAU · PIÈCE
ÉTAGE 1 · Séjour étage 1

TITRE DE LA PLANCHE
Rendus 3D — Séjour étage 1 (3/4)

ÉCHELLE	FORMAT
—	A3
DATE	**INDICE**
11.11.2026	A

424	cote vérifiée (plan source)
≈ 59	cote déduite (relevé)
À CONF.	cote à confirmer

Cotes en cm. Ne pas mesurer sur le dessin. Toutes les cotes sont à vérifier sur site avant exécution.

N° DE DESSIN
KAI-VIL-410

etage1-sejour-04 — Œuvre et bibliothèque M10 (vue de 3/4)

KAÏRA INTERIOR DESIGN

Architecture intérieure

PROJET
Villa — Rez-de-chaussée & Étage 1

DOCUMENT
Dossier technique d'architecture intérieure

NIVEAU · PIÈCE
ÉTAGE 1 · Séjour étage 1

TITRE DE LA PLANCHE
Rendus 3D — Séjour étage 1 (4/4)

ÉCHELLE	FORMAT
—	A3
DATE	**INDICE**
11.11.2026	A

424	cote vérifiée (plan source)
≈ 59	cote déduite (relevé)
À CONF.	cote à confirmer

Cotes en cm. Ne pas mesurer sur le dessin. Toutes les cotes sont à vérifier sur site avant exécution.

N° DE DESSIN
KAI-VIL-411

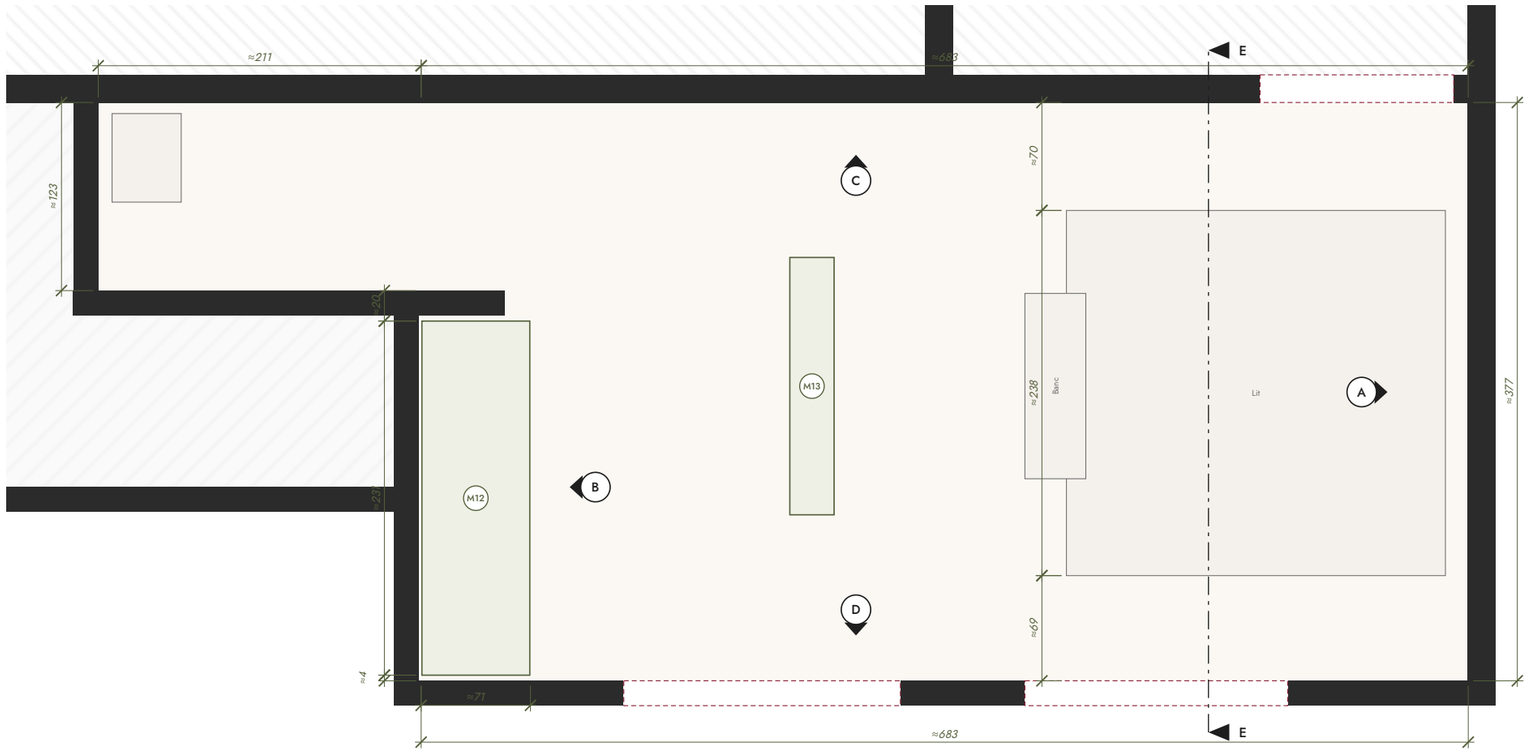

1 PLAN COTÉ — CHAMBRE PRINCIPALE 1:40

CHAMBRE PRINCIPALE

Niveau	ÉTAGE 1
Surface	≈ 28,4 m²
Hauteur sous faux-plafond	≈ 292
Plafond central	**à confirmer**
Sol fini	**à confirmer**

Repères A, B, C… : murs dessinés en élévation. Traits mixtes : coupes. M… : mobilier sur mesure.

KAÏRA INTERIOR DESIGN

KAÏRA INTERIOR DESIGN
Architecture intérieure

PROJET
Villa — Rez-de-chaussée & Étage 1

DOCUMENT
Dossier technique d'architecture intérieure

NIVEAU · PIÈCE
ÉTAGE 1 · Chambre principale

TITRE DE LA PLANCHE
Plan coté — Chambre principale

ÉCHELLE
1:40

FORMAT
A3

DATE
11.11.2026

INDICE
A

424	cote vérifiée (plan source)
≈ 59	cote déduite (relevé)
À CONF.	cote à confirmer

Cotes en cm. Ne pas mesurer sur le dessin. Toutes les cotes sont à vérifier sur site avant exécution.

N° DE DESSIN
KAI-VIL-500

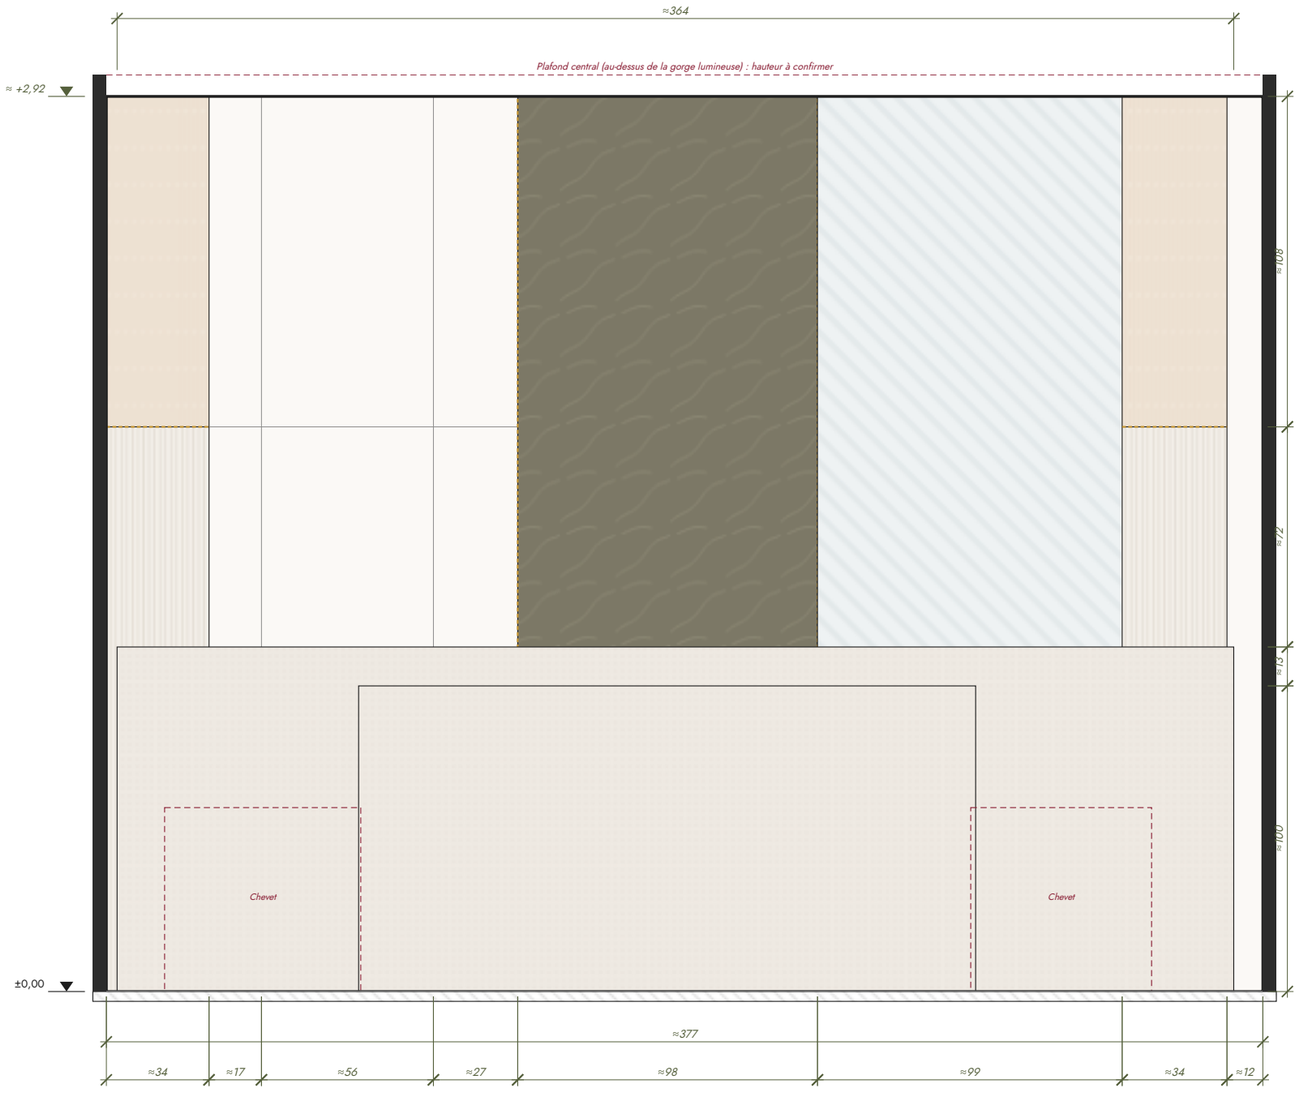

A MUR A — EST (TÊTE DE LIT) 1:20

MUR A — NOTES

- Source : chambre-principale-05. Calibrage : Largeur 377,3 relevée sur la vue de dessus ; hauteur ±5.
- Bande marbre brun-vert veiné rétroéclairée (≈ 98 de large) toute hauteur.
- Tête de lit murale tapissée sur presque toute la largeur ; épaisseur à confirmer.
- Chevets chêne 2 tiroirs : dimensions à confirmer (≈ 60 × 60 ht sur le rendu).

PLAN DE REPÉRAGE

KAÏRA INTERIOR DESIGN

KAÏRA INTERIOR DESIGN
Architecture intérieure

PROJET
Villa — Rez-de-chaussée & Étage 1

DOCUMENT
Dossier technique d'architecture intérieure

NIVEAU · PIÈCE
ÉTAGE 1 · Chambre principale

TITRE DE LA PLANCHE
Élévation A — Chambre principale

ÉCHELLE	FORMAT
1:20	A3
DATE	INDICE
11.11.2026	A

424	cote vérifiée (plan source)
≈ *59*	cote déduite (relevé)
À CONF.	cote à confirmer

Cotes en cm. Ne pas mesurer sur le dessin. Toutes les cotes sont à vérifier sur site avant exécution.

N° DE DESSIN
KAI-VIL-501

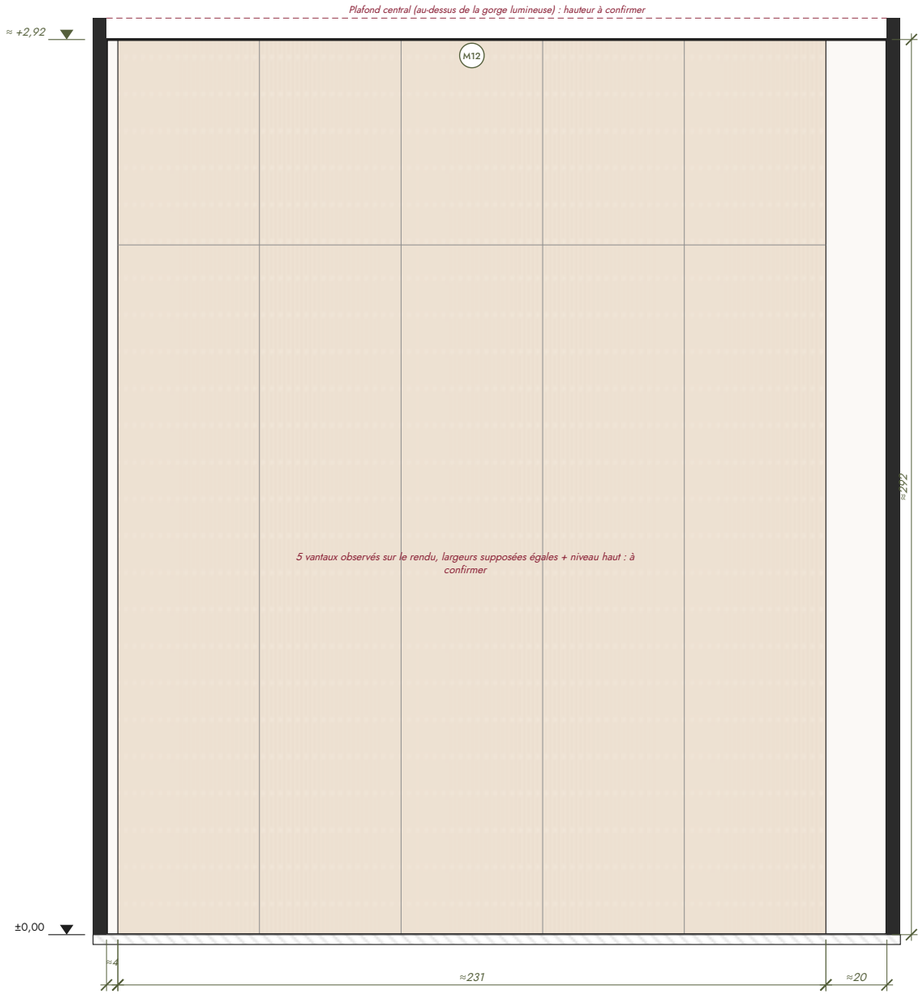

B **MUR B — OUEST (DRESSING)** 1:20

MUR B — NOTES

- Source : chambre-principale-04 (vue de 3/4). Calibrage : Emprise du dressing relevée sur la vue de dessus.
- M12 : dressing chêne ≈ 231 × 70 de profondeur, toute hauteur ; poignées intégrées.
- Hauteur du niveau haut et répartition intérieure à confirmer.

PLAN DE REPÉRAGE

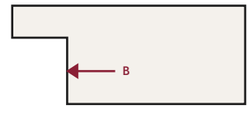

KAÏRA INTERIOR DESIGN

KAÏRA INTERIOR DESIGN
Architecture intérieure

PROJET
Villa — Rez-de-chaussée & Étage 1

DOCUMENT
Dossier technique d'architecture intérieure

NIVEAU · PIÈCE
ÉTAGE 1 · Chambre principale

TITRE DE LA PLANCHE
Élévation B — Chambre principale

ÉCHELLE
1:20

FORMAT
A3

DATE
11.11.2026

INDICE
A

424	cote vérifiée (plan source)
≈ 59	cote déduite (relevé)
À CONF.	cote à confirmer

Cotes en cm. Ne pas mesurer sur le dessin. Toutes les cotes sont à vérifier sur site avant exécution.

N° DE DESSIN
KAI-VIL-502

C — MUR C — NORD (BAIE VITRÉE)

1:30

D — MUR D — SUD (FENÊTRES)

1:30

MUR C — NOTES

- Source : chambre-principale-03 (vue de 3/4). Calibrage : Longueur relevée sur la vue de dessus.
- Baie vitrée près de l'angle nord-est : largeur et hauteur à confirmer.

MUR D — NOTES

- Source : chambre-principale-05 (rideaux). Calibrage : Longueur relevée sur la vue de dessus.
- Baies du mur sud : positions déduites des rideaux ; dimensions à confirmer.

PLAN DE REPÉRAGE

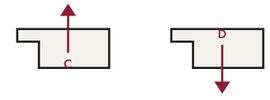

KAÏRA INTERIOR DESIGN

Architecture intérieure

PROJET
Villa — Rez-de-chaussée & Étage 1

DOCUMENT
Dossier technique d'architecture intérieure

NIVEAU · PIÈCE
ÉTAGE 1 · Chambre principale

TITRE DE LA PLANCHE
Élévations C et D — Chambre principale

ÉCHELLE	FORMAT
1:30	A3
DATE	INDICE
11.11.2026	A

424	cote vérifiée (plan source)
≈ 59	cote déduite (relevé)
À CONF.	cote à confirmer

Cotes en cm. Ne pas mesurer sur le dessin. Toutes les cotes sont à vérifier sur site avant exécution.

N° DE DESSIN
KAI-VIL-503

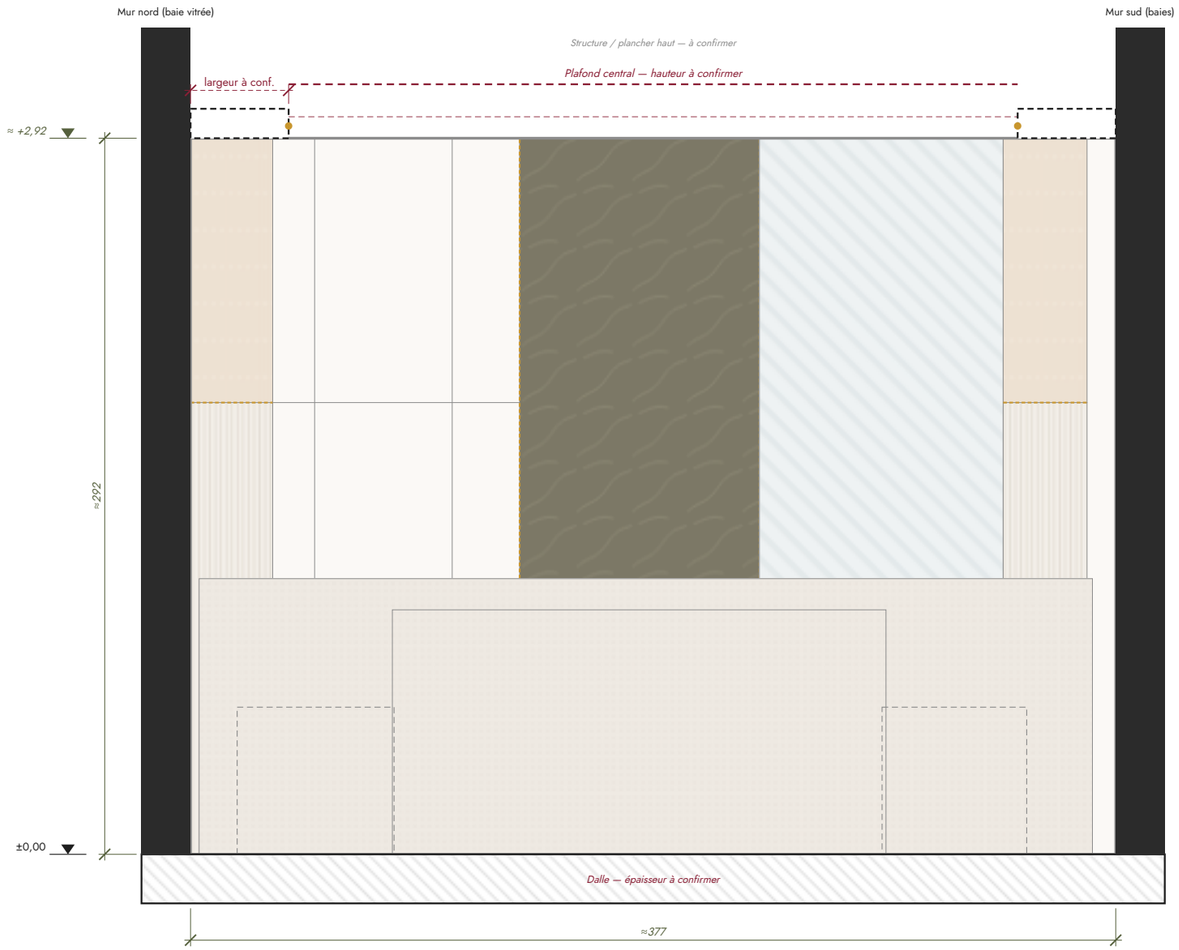

E COUPE EE — CHAMBRE PRINCIPALE (NORD-SUD, VUE VERS L'EST) 1:25

NOTES

- Coupe établie à partir des hauteurs déduites ; l'élévation vue au-delà est dessinée en gris.
- Retombée périphérique de faux-plafond avec gorge lumineuse LED : largeur à confirmer.
- Plafond central, plancher haut et épaisseur de dalle : à confirmer.
- Mobilier coupé : profils relevés (vue de dessus pour la profondeur, rendus pour les hauteurs).

KAÏRA INTERIOR DESIGN

Architecture intérieure

PROJET
Villa — Rez-de-chaussée & Étage 1

DOCUMENT
Dossier technique d'architecture intérieure

NIVEAU · PIÈCE
ÉTAGE 1 · Chambre principale

TITRE DE LA PLANCHE
Coupe EE — Chambre principale

ÉCHELLE
1:25

FORMAT
A3

DATE
11.11.2026

INDICE
A

424	cote vérifiée (plan source)
≈ *59*	cote déduite (relevé)
À CONF.	cote à confirmer

Cotes en cm. Ne pas mesurer sur le dessin. Toutes les cotes sont à vérifier sur site avant exécution.

N° DE DESSIN
KAI-VIL-504

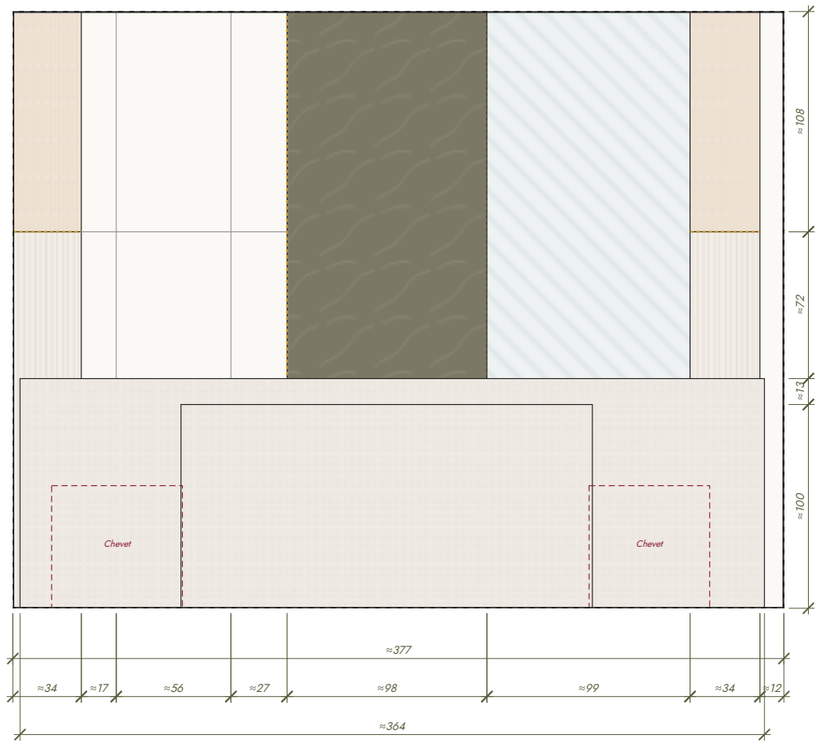

M11 **M11 — VUE DE FACE (EXTRAIT MUR A)** 1:30

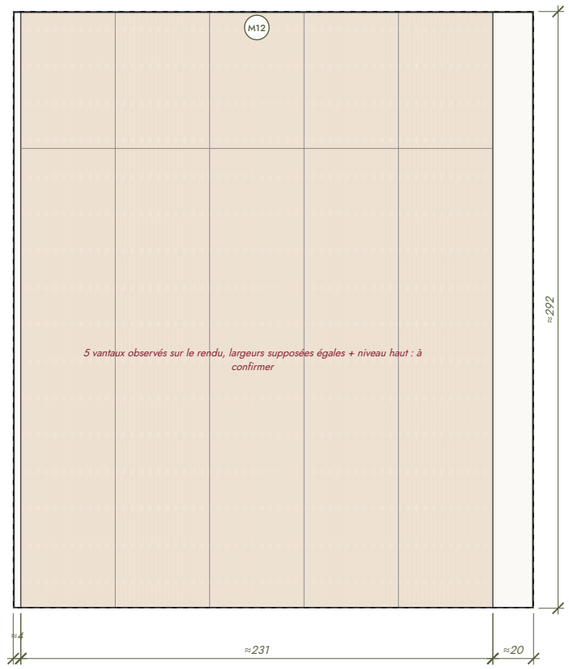

M12 **M12 — VUE DE FACE (EXTRAIT MUR B)** 1:30

NOMENCLATURE DU MOBILIER SUR MESURE

RÉF.	DÉSIGNATION	DIMENSIONS (CM)	OBSERVATIONS
M11	Mur tête de lit : bande marbre, miroirs, colonnes chêne, tête de lit murale	*L ≈ 377 · H ≈ 292 ·* **P à conf.**	tête de lit murale ≈ 364 × 112
M12	Dressing chêne toute hauteur	*L ≈ 231 · P ≈ 70 · H ≈ 292*	5 vantaux + niveau haut
M13	Meuble TV noir mat (îlot face au lit)	*L ≈ 168 · P ≈ 29 ·* **H à conf.**	posé au sol ; hauteur à confirmer

L = longueur, P = profondeur, H = hauteur, pose = hauteur sous meuble. Dimensions ≈ relevées sur la vue de dessus (L, P) et sur les rendus de face (H). Quincaillerie, épaisseurs de panneaux, structure et détails d'assemblage : à définir en plans d'exécution.

KAÏRA INTERIOR DESIGN

KAÏRA INTERIOR DESIGN
Architecture intérieure

PROJET
Villa — Rez-de-chaussée & Étage 1

DOCUMENT
Dossier technique d'architecture intérieure

NIVEAU · PIÈCE
ÉTAGE 1 · Chambre principale

TITRE DE LA PLANCHE
Mobilier sur mesure — Chambre principale

ÉCHELLE
1:30

FORMAT
A3

DATE
11.11.2026

INDICE
A

424 cote vérifiée (plan source)
≈ *59* cote déduite (relevé)
À CONF. cote à confirmer

Cotes en cm. Ne pas mesurer sur le dessin. Toutes les cotes sont à vérifier sur site avant exécution.

N° DE DESSIN
KAI-VIL-505

MATÉRIAUX ET FINITIONS — CHAMBRE PRINCIPALE

	MATÉRIAU	LOCALISATION	TEINTE RELEVÉE	RÉFÉRENCE FABRICANT	FINITION
	Marbre brun foncé veiné	Bande centrale rétroéclairée	#312A1B	**à confirmer**	**à confirmer**
	Tissu clair	Tête de lit murale	#918376	**à confirmer**	**à confirmer**
	Tissu	Banc capitonné	#8D7E6F	**à confirmer**	**à confirmer**
	Chêne	Colonnes, chevets, dressing	#694E39	**à confirmer**	**à confirmer**
	Lames cannelées	Soubassement des colonnes	#A4978A	**à confirmer**	**à confirmer**
—	Miroir	Panneaux à droite de la tête de lit	—	**à confirmer**	**à confirmer**
—	Laiton	Piètement du banc	—	**à confirmer**	**à confirmer**
	Noir	Meuble TV	#19170D	**à confirmer**	**à confirmer**
	Kaki	Linge de lit	#3A3322	**à confirmer**	**à confirmer**
	Rideaux taupe + voilage	Baies	#695E54	**à confirmer**	**à confirmer**

NOTES

- Matériaux identifiés sur les rendus 3D du projet ; aucune référence n'est inventée.
- Teinte relevée : médiane des pixels d'une zone du rendu. Indicative : elle dépend de l'éclairage de la scène.
- « — » : teinte non relevable sur le rendu (reflets, lumière, métal).
- À valider avant commande : échantillons physiques, références fabricants, finitions (mat, satiné, brossé, adouci…), sens du fil et calepinage des panneaux bois et marbre.
- Éclairage : température de couleur et intensité des LED à définir (non mesurables sur les rendus).

KAÏRA INTERIOR DESIGN

Architecture intérieure

PROJET

Villa — Rez-de-chaussée & Étage 1

DOCUMENT

Dossier technique d'architecture intérieure

NIVEAU · PIÈCE

ÉTAGE 1 · Chambre principale

TITRE DE LA PLANCHE

Matériaux et finitions — Chambre principale

ÉCHELLE

—

FORMAT

A3

DATE

11.11.2026

INDICE

A

424 cote vérifiée (plan source)

≈ *59* cote déduite (relevé)

À CONF. cote à confirmer

Cotes en cm. Ne pas mesurer sur le dessin. Toutes les cotes sont à vérifier sur site avant exécution.

N° DE DESSIN

KAI-VIL-506

CHAMBRE PRINCIPALE

Mur A — tête de lit (vue de face)

Fichier : chambre-principale-05.png — rendu 3D original KAÏRA, inséré en entier, sans recadrage ni retouche.

REPÉRAGE — MUR A

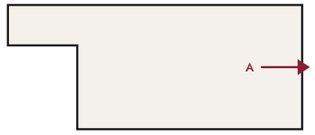

KAÏRA INTERIOR DESIGN

Architecture intérieure

PROJET
Villa — Rez-de-chaussée & Étage 1

DOCUMENT
Dossier technique d'architecture intérieure

NIVEAU · PIÈCE
ÉTAGE 1 · Chambre principale

TITRE DE LA PLANCHE
Rendu 3D — Chambre principale

ÉCHELLE	FORMAT
—	A3
DATE	INDICE
11.11.2026	A

424	cote vérifiée (plan source)
≈ *59*	cote déduite (relevé)
À CONF.	cote à confirmer

Cotes en cm. Ne pas mesurer sur le dessin. Toutes les cotes sont à vérifier sur site avant exécution.

N° DE DESSIN
KAI-VIL-507

chambre-principale-01 — Mur A — tête de lit (vue de 3/4)

chambre-principale-02 — Mur A — variante de cadrage

KAÏRA
INTERIOR DESIGN

KAÏRA INTERIOR DESIGN
Architecture intérieure

PROJET
Villa — Rez-de-chaussée & Étage 1

DOCUMENT
Dossier technique d'architecture intérieure

NIVEAU · PIÈCE
ÉTAGE 1 · Chambre principale

TITRE DE LA PLANCHE
Rendus 3D — Chambre principale (1/2)

ÉCHELLE	FORMAT
—	A3
DATE	**INDICE**
11.11.2026	A

424	cote vérifiée (plan source)
≈ 59	cote déduite (relevé)
À CONF.	cote à confirmer

Cotes en cm. Ne pas mesurer sur le dessin. Toutes les cotes sont à vérifier sur site avant exécution.

N° DE DESSIN
KAI-VIL-508

chambre-principale-03 — Vue large avec la baie vitrée du mur C

chambre-principale-04 — Mur B — dressing M12 et meuble TV M13

KAÏRA
INTERIOR DESIGN

KAÏRA INTERIOR DESIGN
Architecture intérieure

PROJET
Villa — Rez-de-chaussée & Étage 1

DOCUMENT
Dossier technique d'architecture intérieure

NIVEAU · PIÈCE
ÉTAGE 1 · Chambre principale

TITRE DE LA PLANCHE
Rendus 3D — Chambre principale (2/2)

ÉCHELLE	FORMAT
—	A3
DATE	**INDICE**
11.11.2026	A

424	cote vérifiée (plan source)
≈ 59	cote déduite (relevé)
À CONF.	cote à confirmer

Cotes en cm. Ne pas mesurer sur le dessin. Toutes les cotes sont à vérifier sur site avant exécution.

N° DE DESSIN
KAI-VIL-509

POINTS GÉNÉRAUX À RELEVER SUR SITE

- Niveau du plancher de l'étage 1, hauteur d'étage et épaisseurs de dalles.
- Hauteur des plafonds centraux au-dessus des gorges lumineuses (4 pièces).
- Largeur des retombées de faux-plafond (chambre d'amis, séjour et chambre de l'étage).
- Sens d'ouverture de toutes les portes.
- Étage 1 : vérification sur site de toutes les cotes déduites de la vue de dessus (aucun plan coté).
- Étage 1 : nombre, positions, largeurs, allèges et linteaux des baies.
- RDC : nature des segments 85,8 / 142 / 163 du mur d'escalier (plan source).
- Chambre d'amis : placard « 130 » du plan source absent de la maquette 3D.

PIÈCE	REPÈRE	ÉLÉMENT À CONFIRMER
Séjour RDC	Mur A	Plafond central au-dessus de la gorge lumineuse : hauteur à confirmer.
Séjour RDC	Mur A	Panneaux chêne arrondis rétroéclairés : épaisseur à confirmer.
Séjour RDC	Mur B	Grand tableau (personnage au chapeau) : position et dimensions à confirmer
Séjour RDC	Mur B	Nature des segments 85,8 / 142 / 163 du plan source : à confirmer
Séjour RDC	Mur C	Console : longueur ≈ 128, profondeur ≈ 30 (vue de dessus). Hauteur de pose à confirmer.
Séjour RDC	Mur C	Colonne marbre veiné + console : dimensions à confirmer
Séjour RDC	Mur D1	M3 : bibliothèque chêne toute hauteur, profondeur ≈ 23 ; répartition des étagères à confirmer.
Séjour RDC	Mur D1	Œuvre rouge : bas ≈ 90, haut ≈ 217 ; largeur à confirmer (rendu 09 partiel).
Séjour RDC	Mur D2	Porte d'entrée : ≈ 163 × 235, deux vantaux bois foncé, sens d'ouverture à confirmer.
Séjour RDC	Mur D2	M5 : colonnes chêne (×3) ≈ 61 de large, partie basse cannelée, ligne LED à ≈ 105 ; profondeur à confirmer.
Séjour RDC	Mur E	Fenêtres F1 et F2 : largeurs relevées sur le plan source ; allège et linteau à confirmer.
Séjour RDC	Mur E	Œuvre posée en partie basse (bas ≈ 21) : fixation à confirmer.
Séjour RDC	Mur E	F2 : allège et linteau.
Séjour RDC	Mur E	F1 : allège et linteau.
Chambre d'amis	Mur A	Lames chêne verticales toute hauteur ; profil et pas des lames à confirmer.
Chambre d'amis	Mur A	Fente miroir verticale (≈ 6 cm) : épaisseur et fixation à confirmer.
Chambre d'amis	Mur B	Fenêtre F5 : largeur relevée sur le plan source ; allège et linteau à confirmer.
Chambre d'amis	Mur B	F5 : allège et linteau.
Chambre d'amis	Mur C	M7 : coiffeuse suspendue chêne, plateau marbre ; hauteur de plateau à confirmer (≈ 80-85).
Chambre d'amis	Mur D	Aucun rendu de ce mur : traitement et hauteur de l'ouverture à confirmer.
Chambre d'amis	Mur D	Placard « 130 » du plan source non représenté dans la maquette 3D : à confirmer.
Chambre d'amis	Mur D	M8 — armoire de l'alcôve (en retrait)
Séjour étage 1	Mur B	Porte double : ≈ 156 × 208, deux oculus vitrés verticaux ; sens d'ouverture à confirmer.
Séjour étage 1	Mur C	Baies du mur sud : positions déduites des rideaux de la maquette ; largeurs, allèges et linteaux à confirmer.
Séjour étage 1	Mur D	Nombre, largeurs et hauteurs des baies du mur ouest : à confirmer.
Chambre principale	Mur A	Tête de lit murale tapissée sur presque toute la largeur ; épaisseur à confirmer.
Chambre principale	Mur A	Chevets chêne 2 tiroirs : dimensions à confirmer (≈ 60 × 60 ht sur le rendu).
Chambre principale	Mur B	Hauteur du niveau haut et répartition intérieure à confirmer.
Chambre principale	Mur B	5 vantaux observés sur le rendu, largeurs supposées égales + niveau haut : à confirmer
Chambre principale	Mur C	Baie vitrée près de l'angle nord-est : largeur et hauteur à confirmer.
Chambre principale	Mur D	Baies du mur sud : positions déduites des rideaux ; dimensions à confirmer.
Séjour RDC	M2	Mur TV : colonne cannelée, miroir, panneaux chêne arrondis rétroéclairés, colonne à niches : P à confirmer.
Séjour RDC	M4	Console murale + colonne marbre (mur est) : H à confirmer.
Chambre d'amis	M7	Coiffeuse suspendue chêne, plateau marbre + miroir : P à confirmer.
Chambre d'amis	M8	Armoire de l'alcôve : H à confirmer.
Séjour étage 1	M9b	Étagère verticale éclairée, montant marbre : P à confirmer.
Chambre principale	M11	Mur tête de lit : bande marbre, miroirs, colonnes chêne, tête de lit murale : P à confirmer.
Chambre principale	M13	Meuble TV noir mat (îlot face au lit) : H à confirmer.

KAÏRA INTERIOR DESIGN

KAÏRA INTERIOR DESIGN
Architecture intérieure

PROJET
Villa — Rez-de-chaussée & Étage 1

DOCUMENT
Dossier technique d'architecture intérieure

NIVEAU · PIÈCE
Général · Synthèse

TITRE DE LA PLANCHE
Récapitulatif des cotes et éléments à confirmer

ÉCHELLE
—

FORMAT
A3

DATE
11.11.2026

INDICE
A

424 cote vérifiée (plan source)
≈ 59 cote déduite (relevé)
À CONF. cote à confirmer

Cotes en cm. Ne pas mesurer sur le dessin. Toutes les cotes sont à vérifier sur site avant exécution.

N° DE DESSIN
KAI-VIL-900